
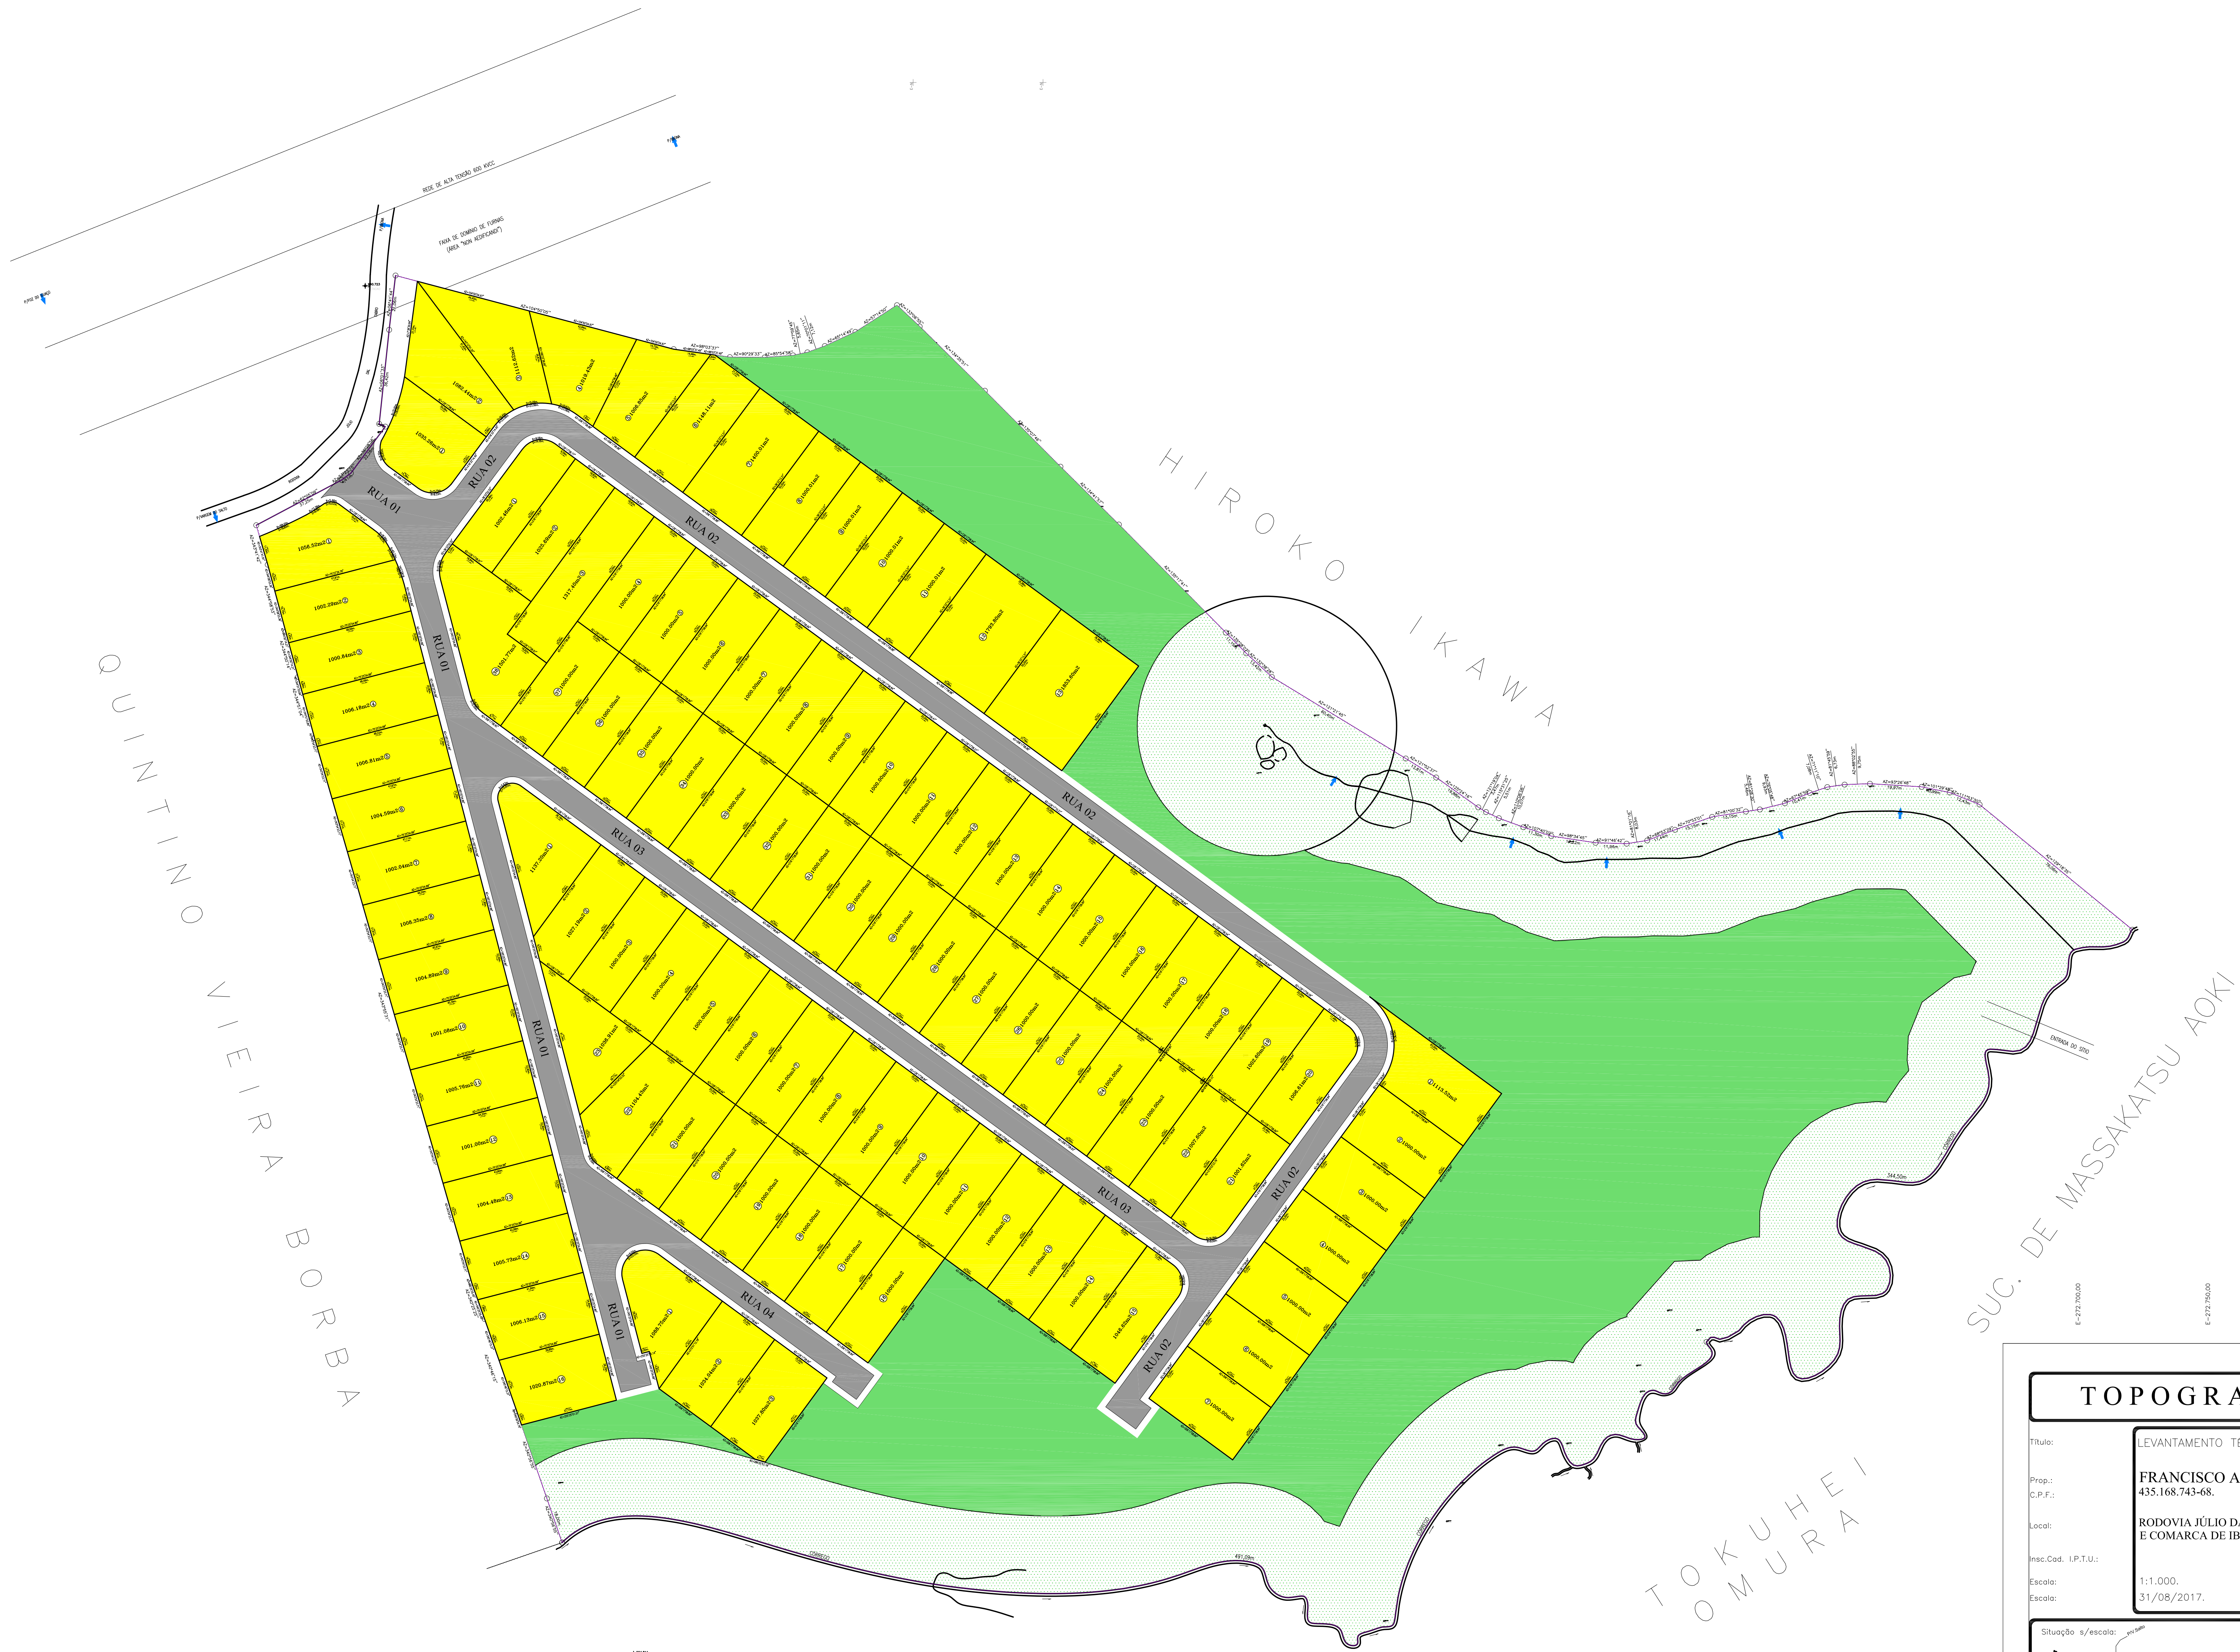


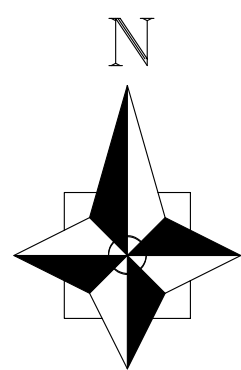

SUC. DE QUINTINO VIEIRA BORBA
E ANTONIO GODINHO DIAS

TOPOGRAFIA

FOLHA ÚNICA

Título: LEVANTAMENTO TÉCNICO TOPOGRÁFICO.

Prop.: FRANCISCO ALBERTO DE MESQUITA ALVES.
C.P.F.: 435.168.743-68.

Lote: RODOVIA JÚLIO DAL FABRO - BAIRRO DO CUPIM - MUNICÍPIO E COMARCA DE IBIÚNA - SÃO PAULO.

Insc. Cad. I.P.T.U.: 31/08/2017.

Escala: 1:1.000.

Escala: 31/08/2017.

Situação s/escala:

Declaro que a aprovação do projeto, não implica no reconhecimento por parte da Prefeitura do direito de propriedade do terreno.

Prop.: Francisco Alberto de Mesquita Alves.

Áreas:	
MAT.1.505/AV.5	123.734,605 m².
MAT.9.965	94.952,83 m².
ÁREA TOTAL	218.687,435 m².

Declaro Grangeria Neto.
Agrimensor - CREASP.506.187.571-4.
Responsável Técnico.
A.5.12 - 28527230172358321.

Rua José Coelho, Ramalho-185-Centro-Ibiúna-SP - (15) 93610-0814-e-mail:grangeria1@gmail.com